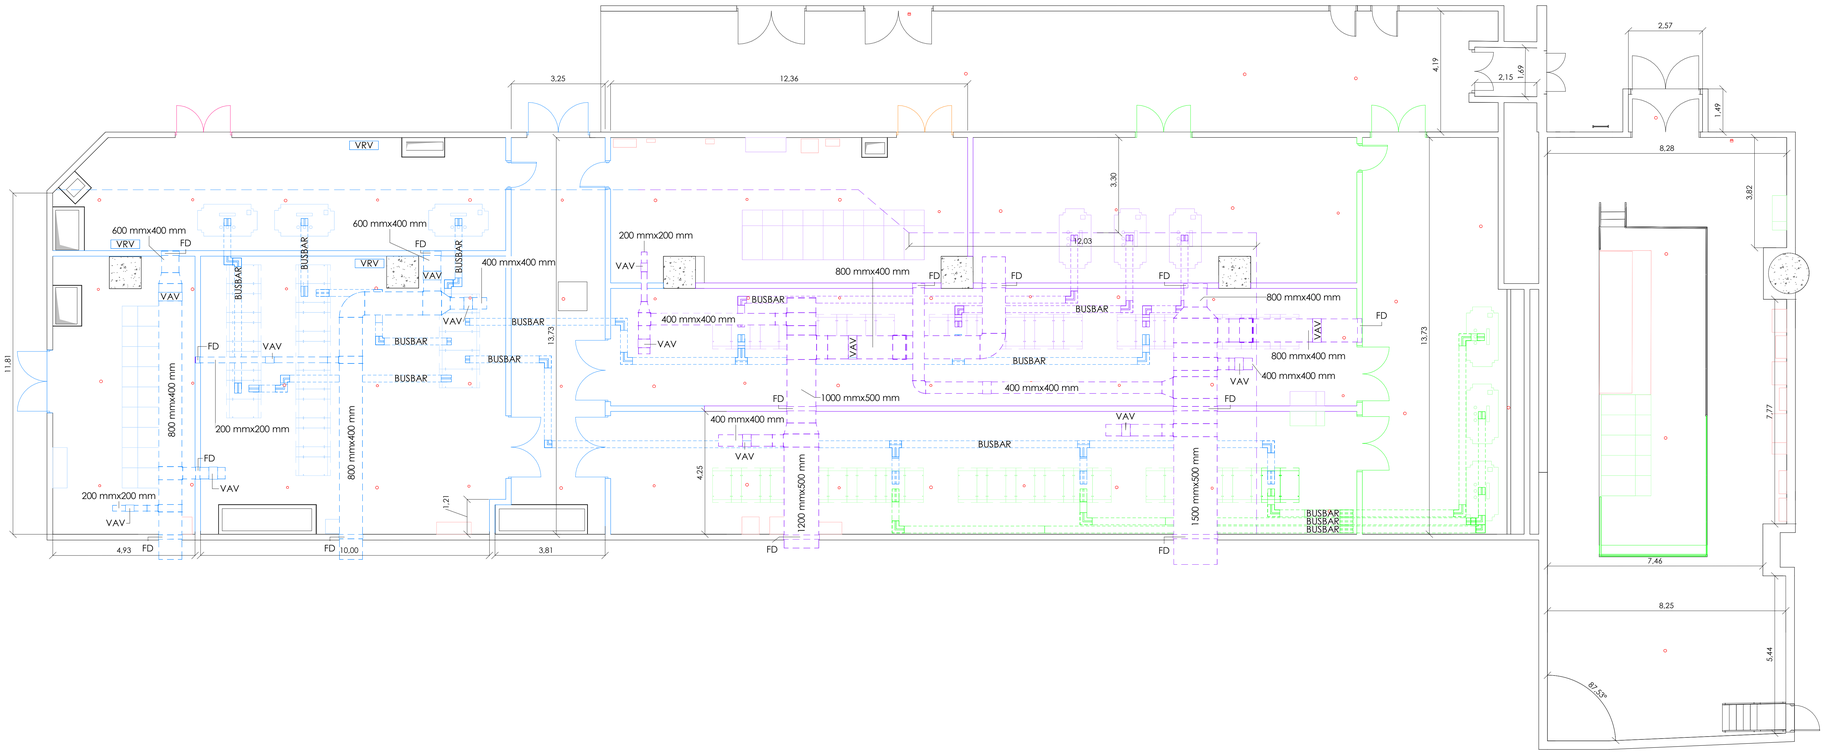

O3149-IPS-20B-1048-DW-T1-T2-T5-T7_BUSBAR AND HVAC LAYOUT

1 : 75

LEGENDS:

- Phase-1
- Phase-2
- Phase-3
- Phase-4
- Phase-5
- Phase-6

FD — Fire Damper

VAV — Variable Air Volume

— Floor Opening

— Fire Alarm Device

VRV — Variable Refrigerant Volume

REV	DATE	CHANGE
1	26-02-2026	BASIC DESIGN

PROJECT

Brussels Airport

Substation Replacement

Leopoldlaan, 1930 Zaventem, Belgium

AUTHOR

Group - IPS
Industrial Projects Services

GROUP-IPS
Avenue R. Schuman, 42
B - 1410 Nivelles

Phone : +32 (0)67 87 43 70
Fax : +32 (0)67 87 40 80

ips@group-ips.be

CUSTOMER

brussels airport
the heart of Europe

ARCHITECT

CONTRACTOR

PROJECT NUMBER	O3140
PROJECT PHASE	Basic Design
DOCUMENT NAME	O3149-TAL-BA-TN-M3-ARC_MEP-ELECTRICAL EQUIPMENT AND BUSBAR LAYOUT
CUSTOMER REFERENCE	
AUTHOR	Jesus Egido
CHECKER	Gary D'Ursel
APPROBATOR	Bram Puttemans
VALIDATOR	Dimitri De Schrijver
SERVICE	
ARCHITECT	
TASK	
REGISTER	
SCALE	1 : 75
PAPER	A0
DATE	26-02-2026
REVISION	1

This drawing is property of IPS and may not be reproduced or modified with its written official permission